


A20 SM-A205 FINGERPRINT

DIGITAL BOARD ESQUEMAS DIGITALIZADOS

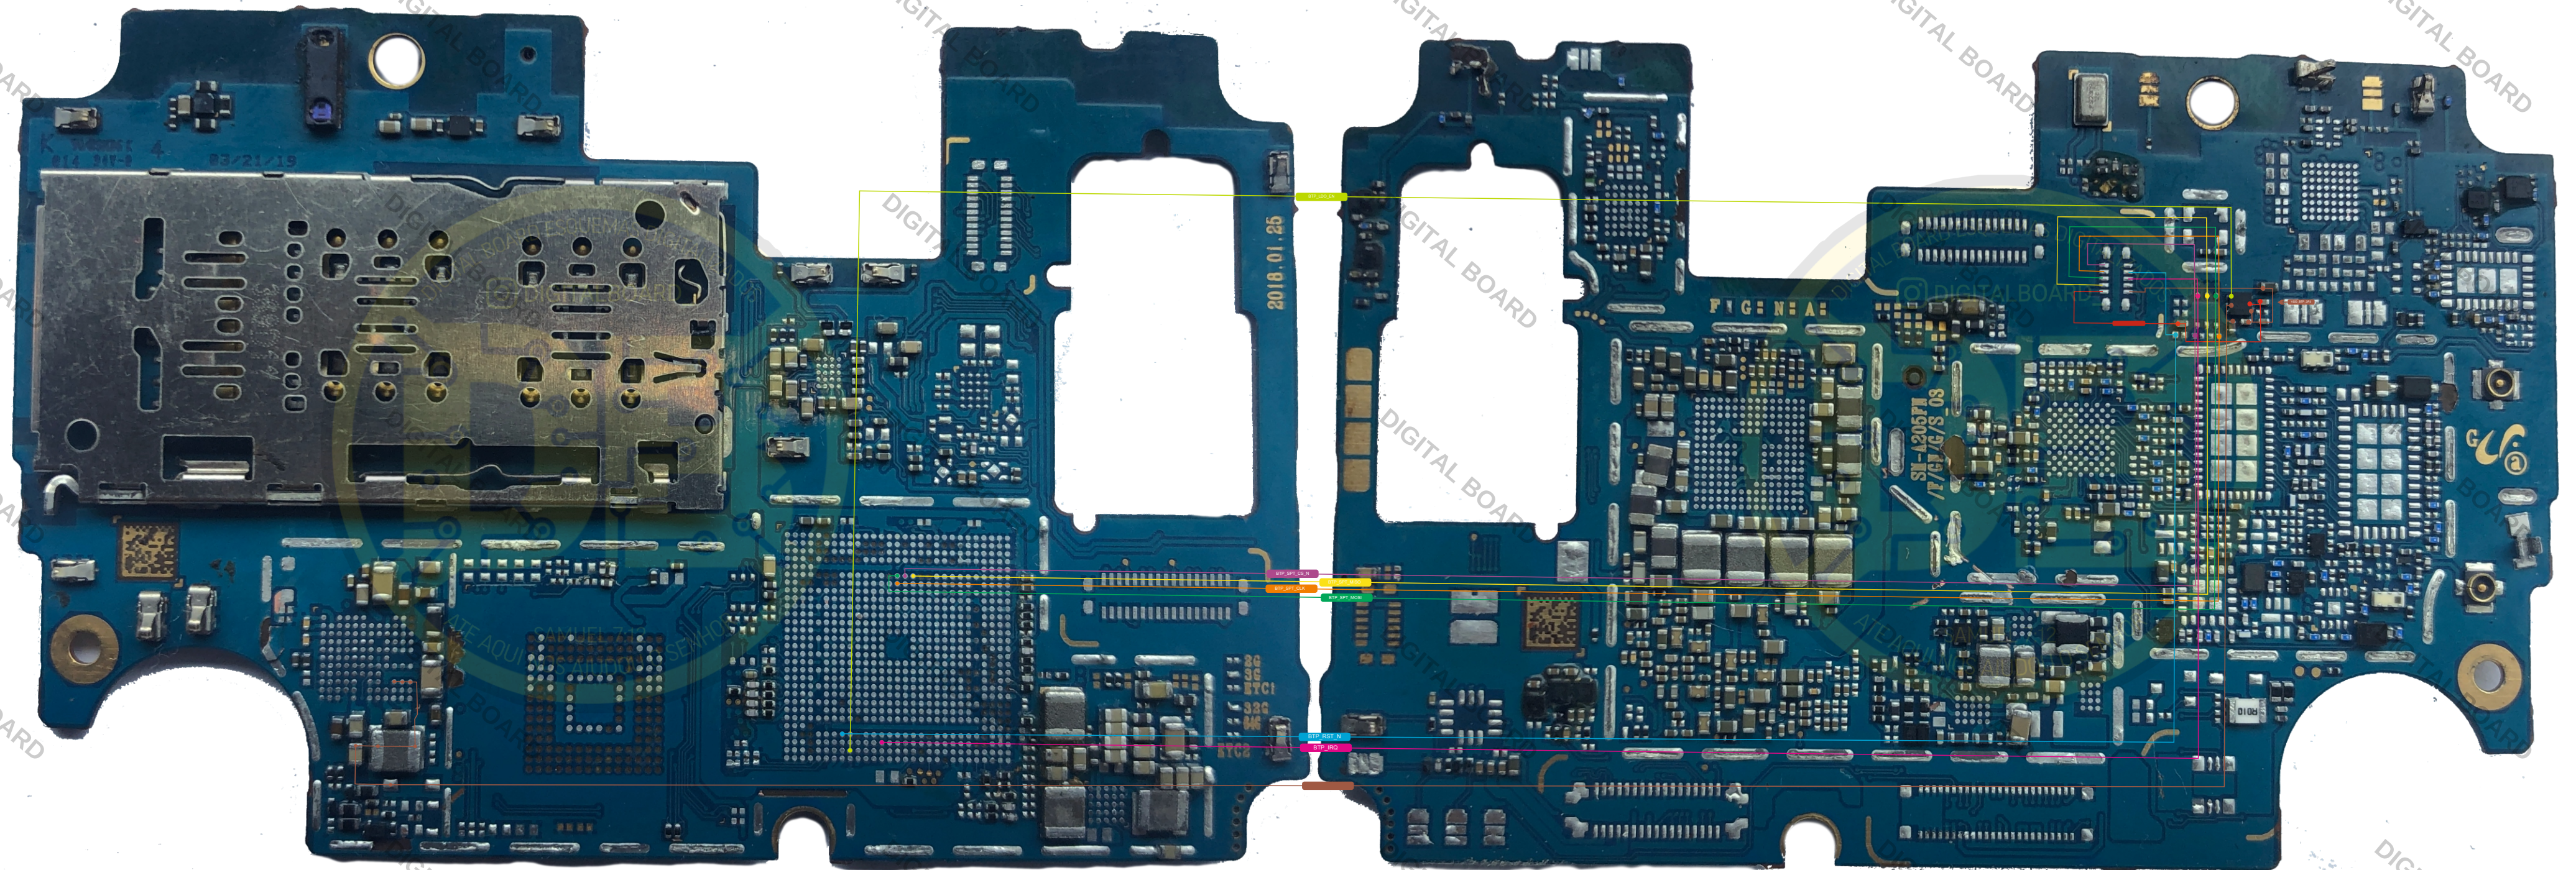

VDD_BTP_3P3

BTP_LDO_EN

BTP_SPT_CS_N

BTP_SPT_MISO

BTP_SPT_CLK

BTP_SPT_MOSI

BTP_RST_N

BTP_IRQ