


A21S SM-A217 FINGERPRINT

DIGITAL BOARD ESQUEMAS DIGITALIZADOS

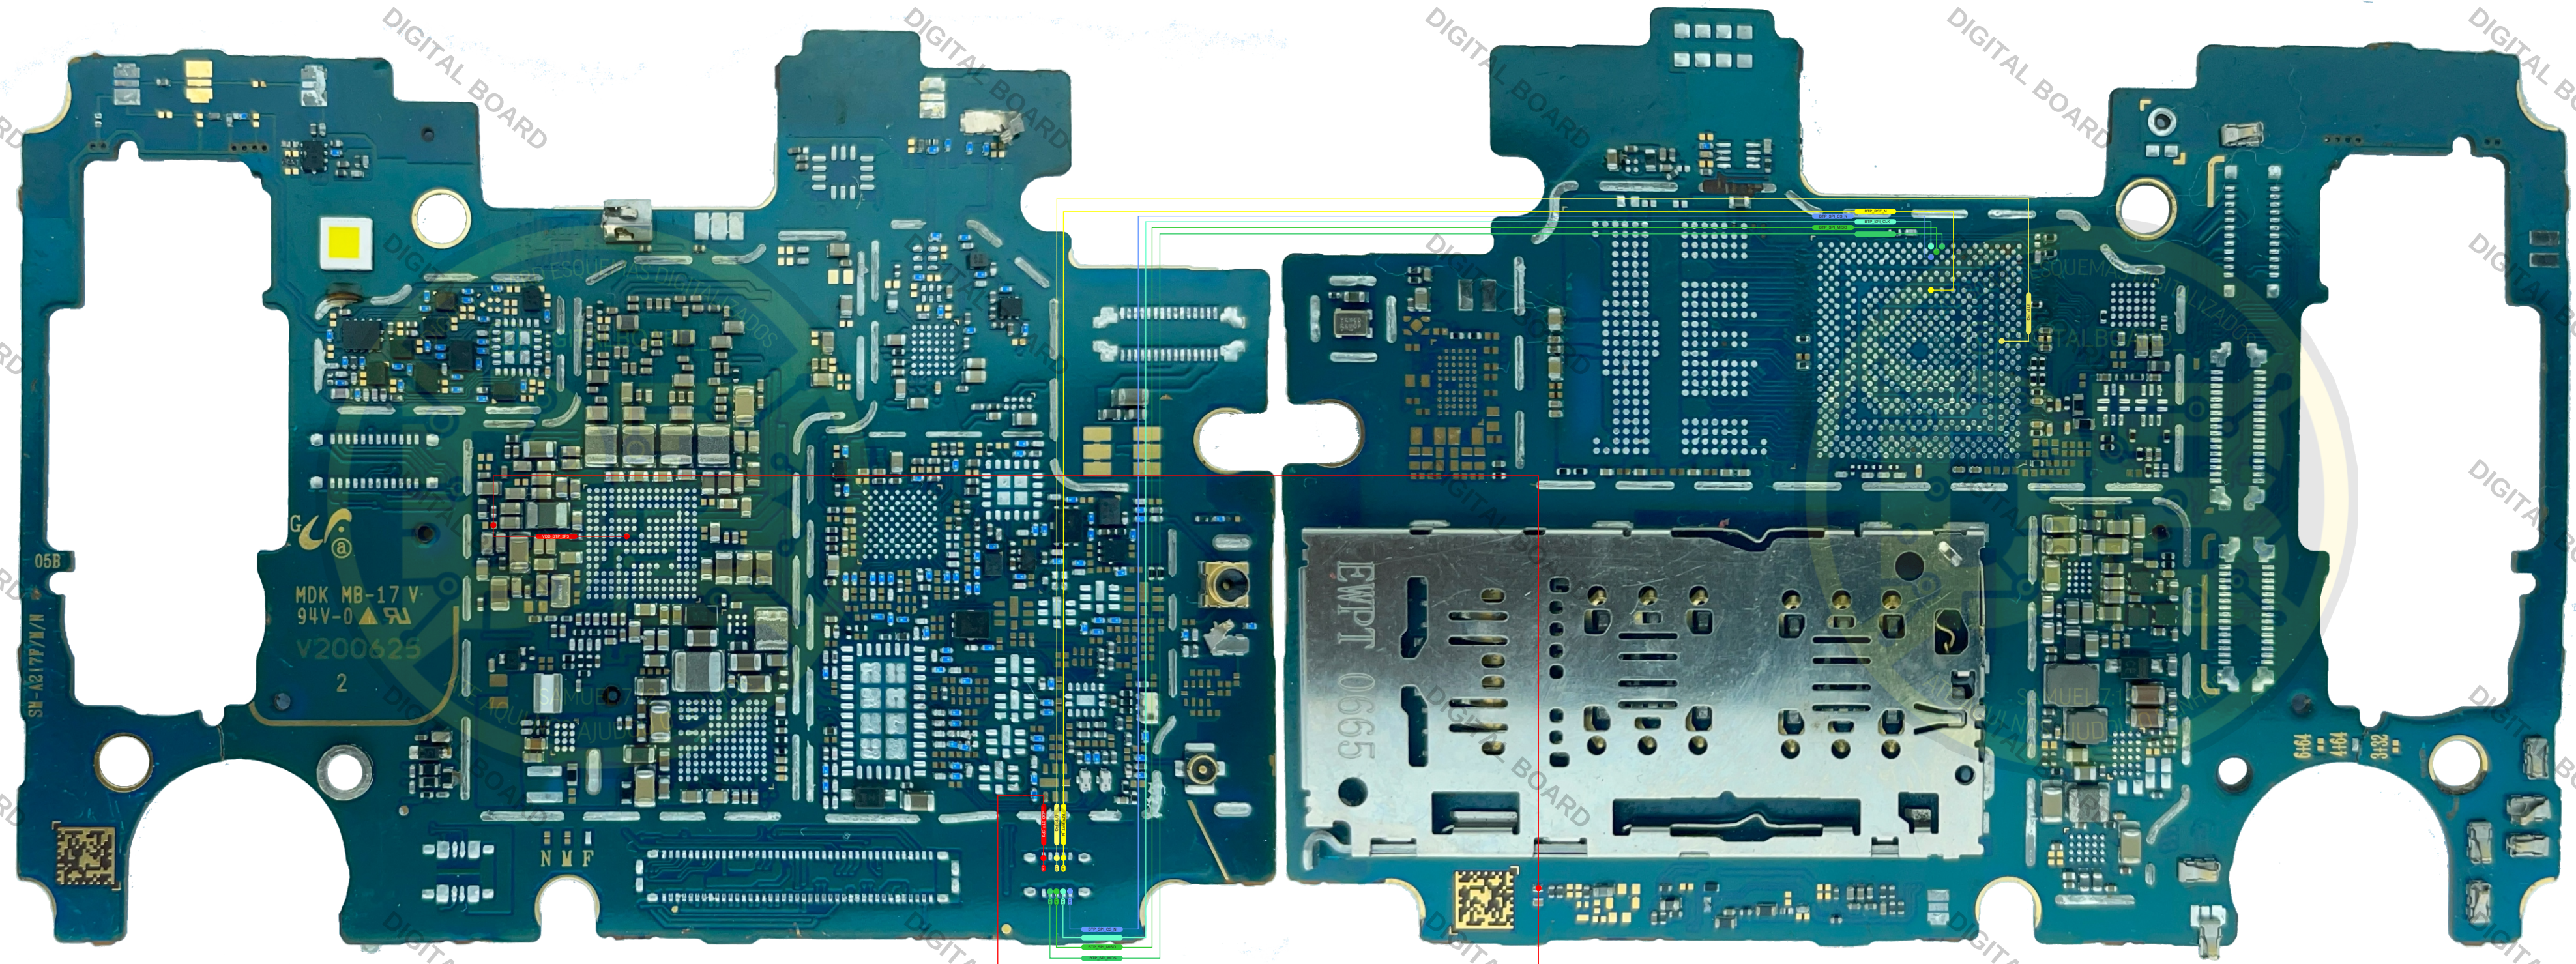

VDD_BTP_3P3

BTP_RST_N

BTP_SPI_CLK

BTP_SPI_CS_N

BTP_SPI_MISO