


A30 SM-A305 FINGERPRINT

DIGITAL BOARD ESQUEMAS DIGITALIZADOS

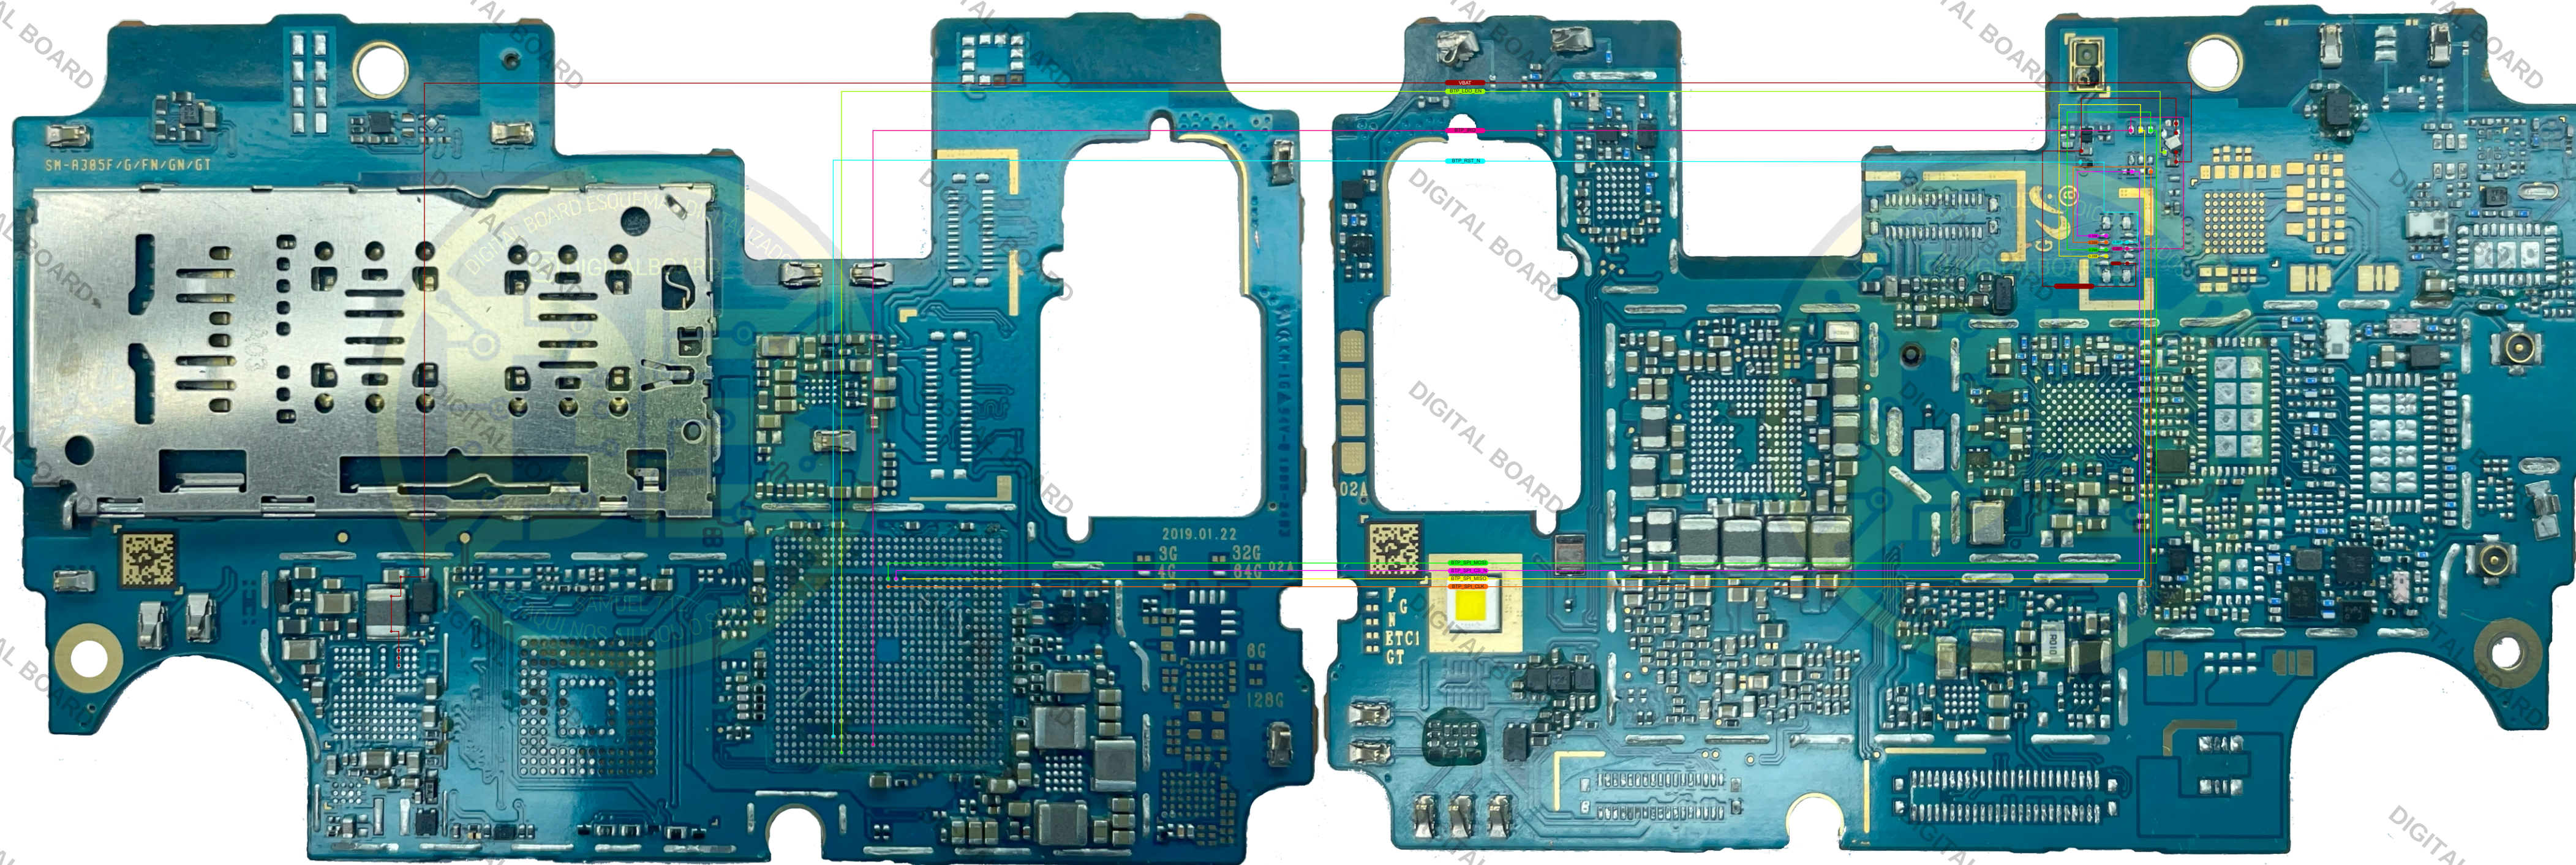

VBAT

BTP_LDO_EN

BTP_IRQ

BTP_RST_N

WHATSAPP/TELEGRAM +55 (33) 98444-4376